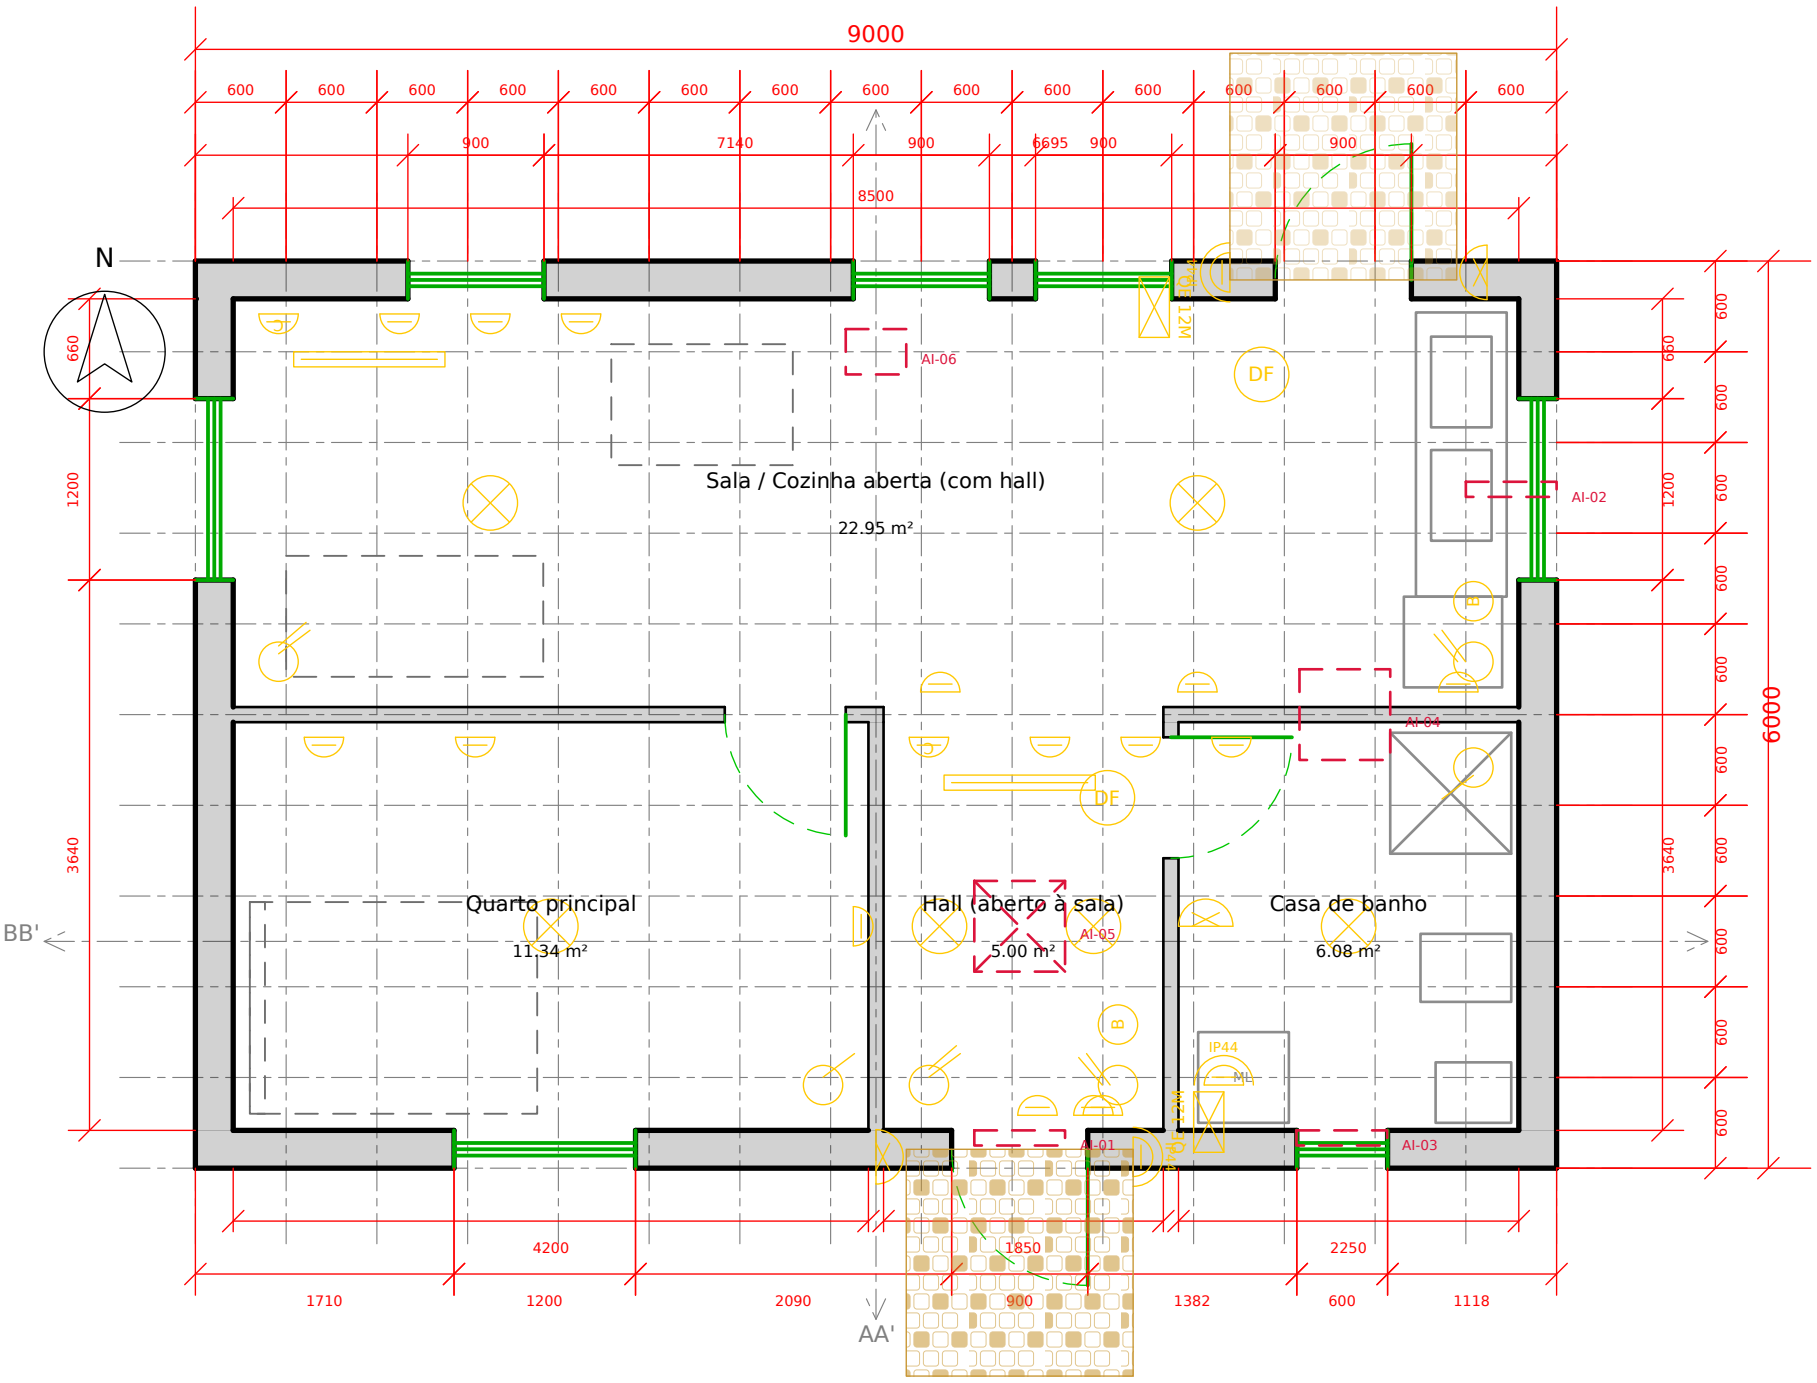

MEP-ELE: símbolos IEC 60617 / NP 1101. Esquema unifilar e ficha TRIE (não publicada).

n/a (documentação de referência, sem autor de projecto) — Versão: selo c2d1ffeb79f1 · Data: 2026-10-15

Doitms Casa DC-T1 — Planta

doitms
casa

9.0 × 6.0 m · 54 m² bruta · ~45.4 m² útil · 1 quarto + sala/cozinha aberta + WC · 2 saídas

SKU: DC-T1 Variante: continente	Prancha: Planta Escala: 1:50	Norte: ↑ Y Sistema: SI · m / mm	N.º DA.01 Folha 1/11

Licença: CC BY-SA 4.0
Não é projecto nem tem termo de responsabilidade; não construir sem profissionais habilitados.