# Esquema unifilar — Casa Base T1 — quadro principal QE-01

Monofásico 230 V · P contratada: 6.90 kVA · IG bipolar 40 A · Diferencial geral 30 mA Classe A




**Notas técnicas — TRIE / CERTIEL:**

· Quadro QE-01 — 12 módulos DIN.
· Esquema de ligação à terra: TT (terra própria por eléctrodo verniz cobreado L=2 m + PE 6 mm² Cu).
· Disjuntor geral diferencial 30 mA Classe A + IG bipolar.
· Sismicidade: recomenda-se IG acessível a menos de 2 m do chão.
· Etiquetagem colorida Doitms (convenção interna) — ver legenda no canto inferior direito + CSV etiquetas-quadro-DC-T1.csv para impressão TRIE.


n/a (documentação de referência, sem autor de projecto)
Variante: continente
Folha 11/11
Versão: selo c2d1ffeb79f1
Data: 2026-10-15


Licença: CC BY-SA 4.0

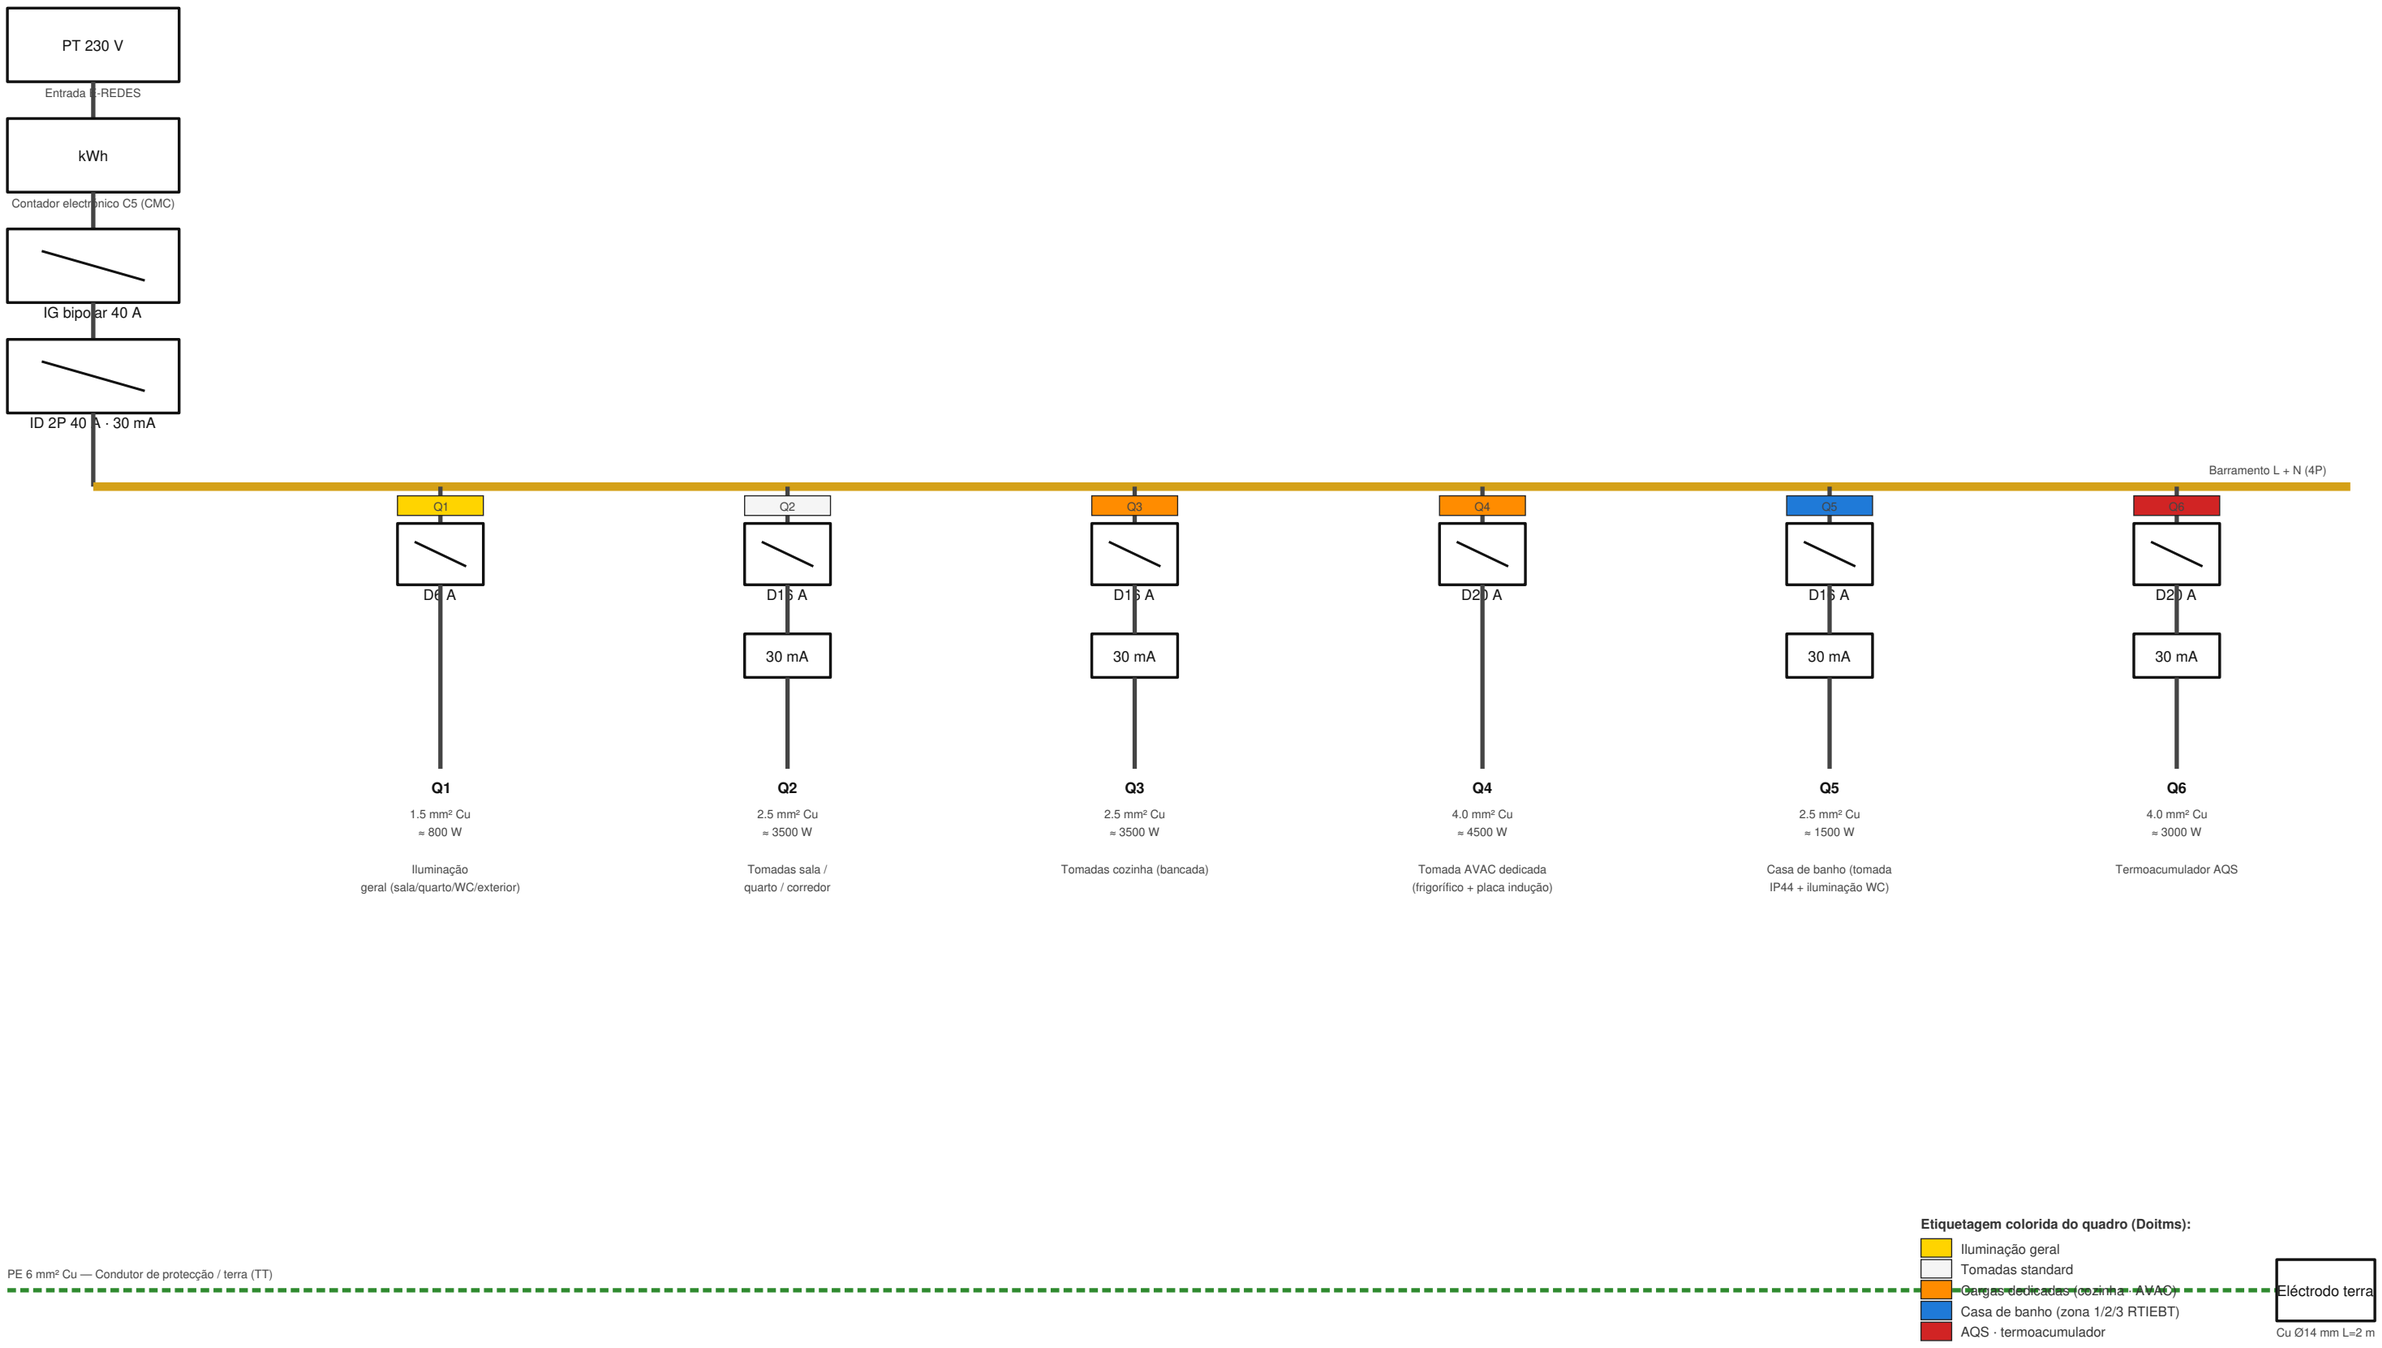

Não é projecto nem tem termo de responsabilidade; não construir sem profissionais habilitados.